



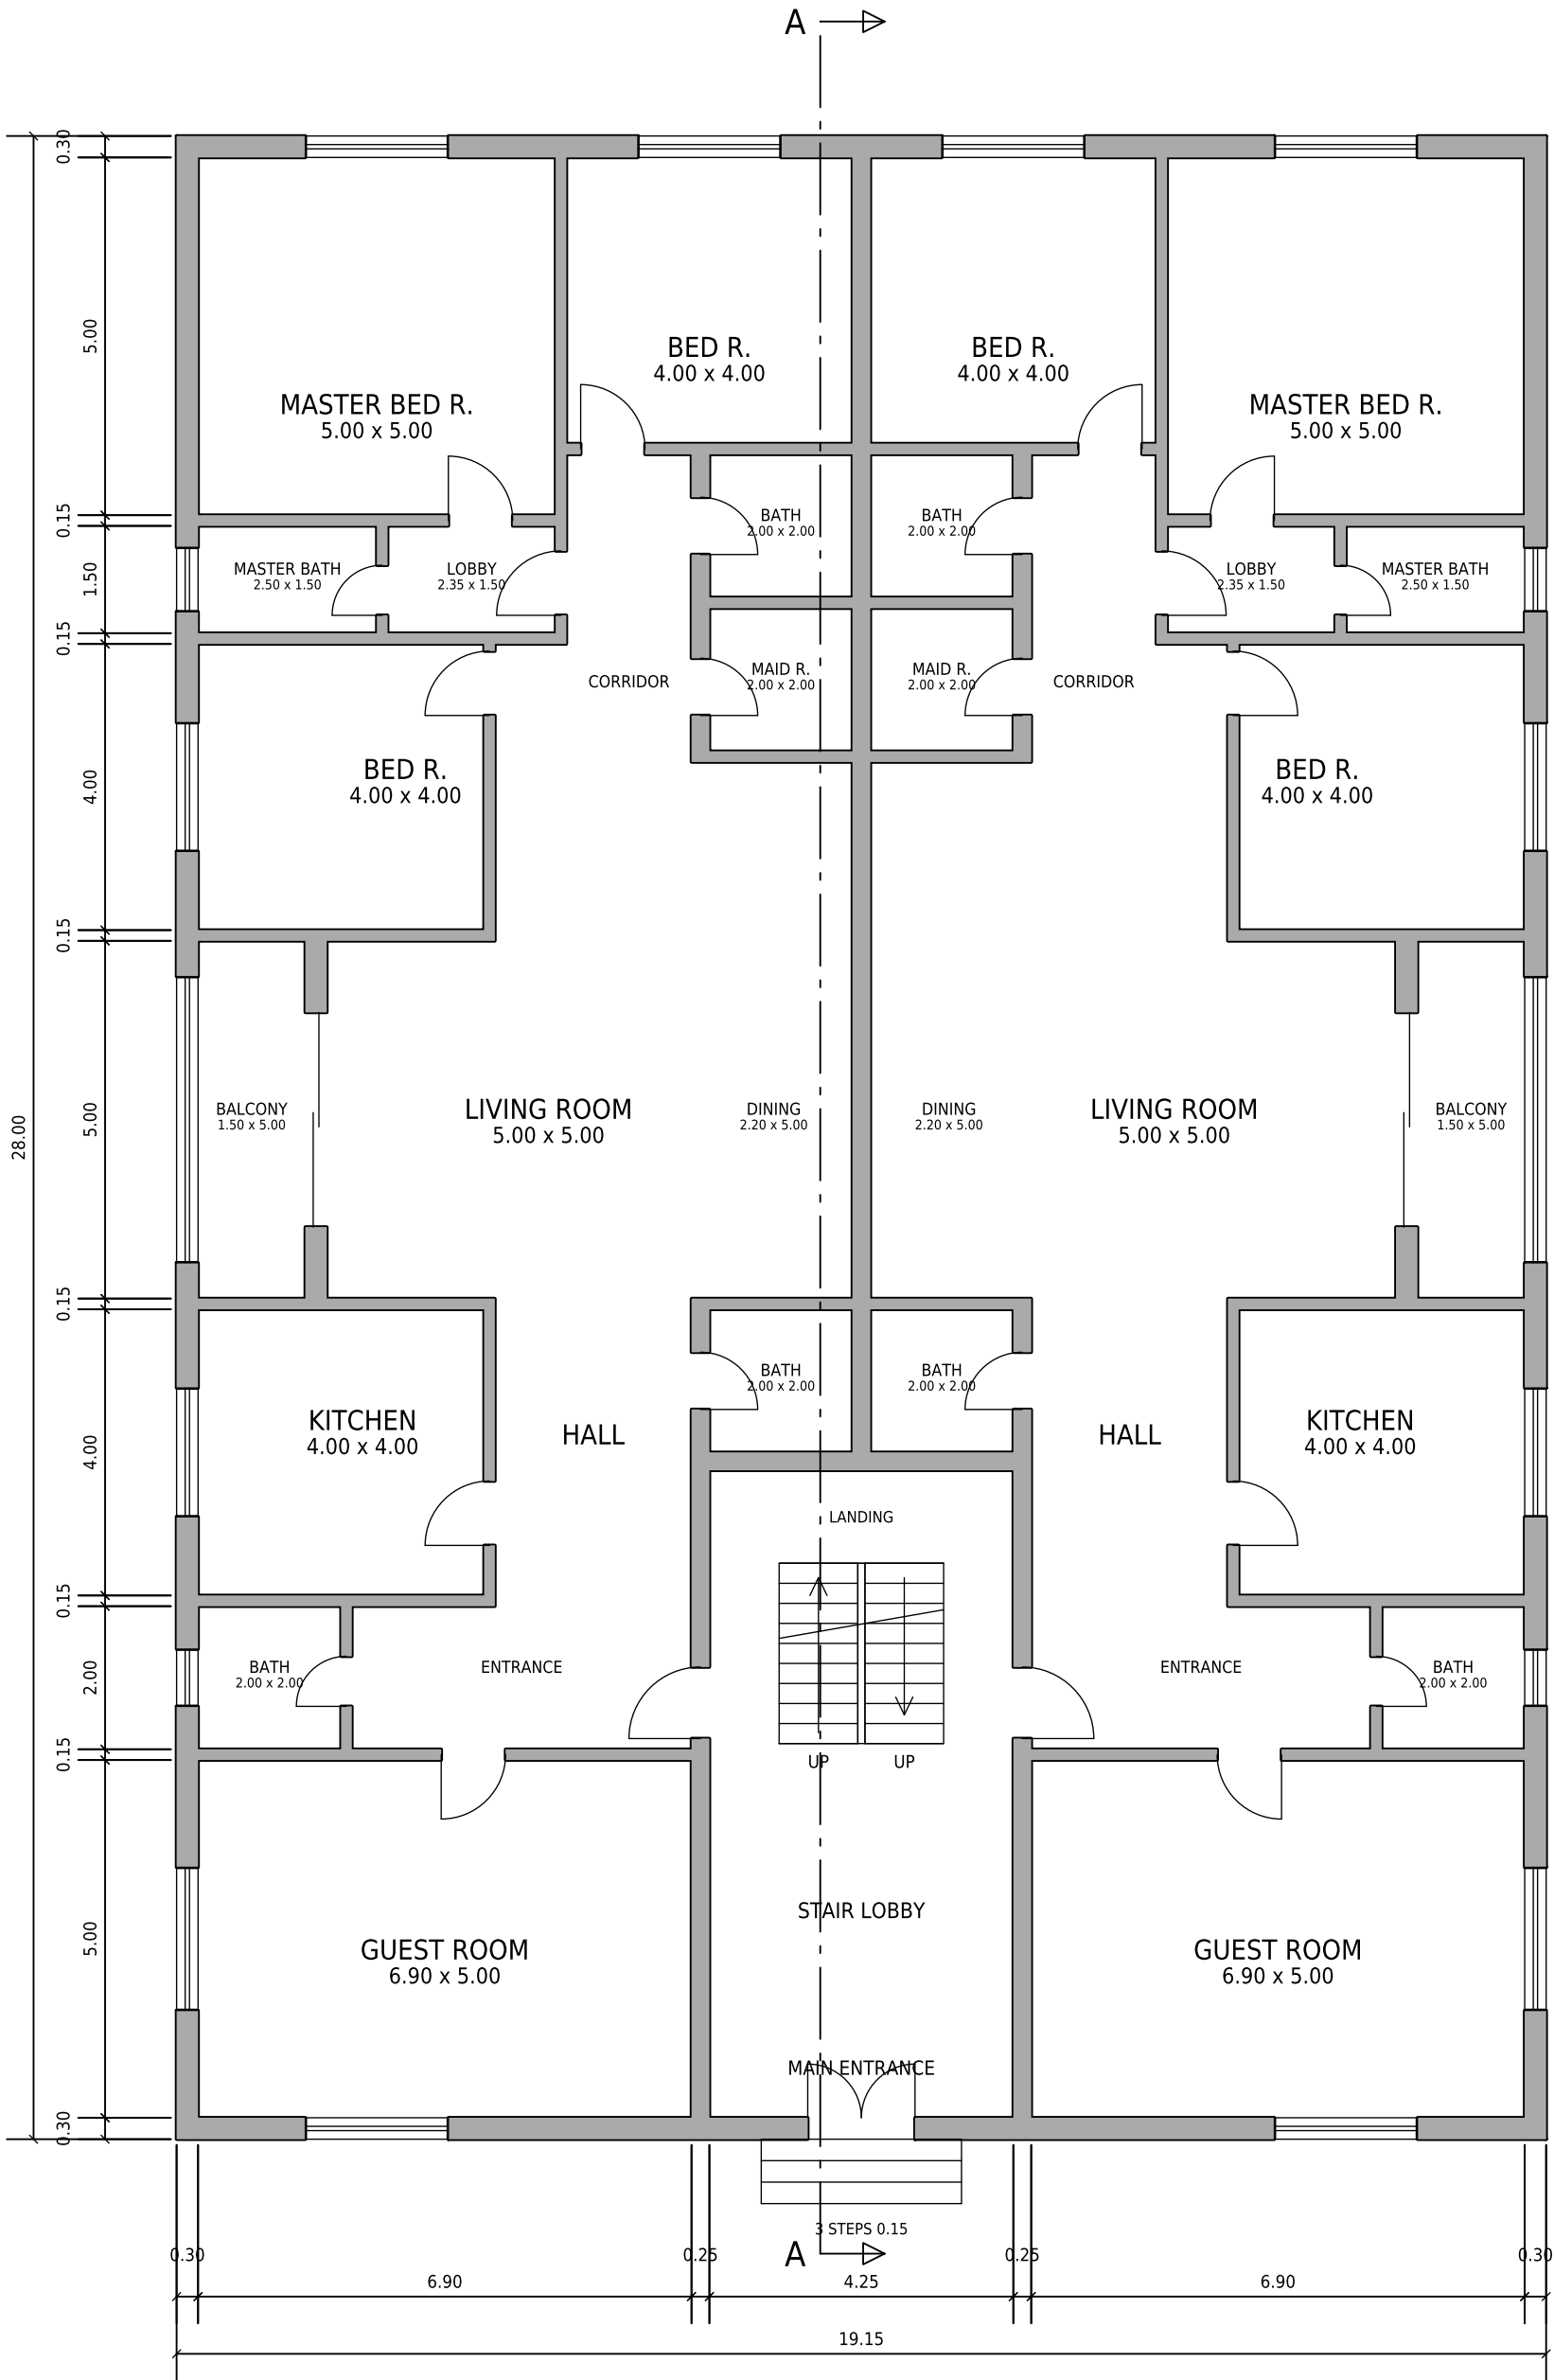


GROUND FLOOR PLAN

FFL ±0.00 | Scale 1:100 | 2 apartments

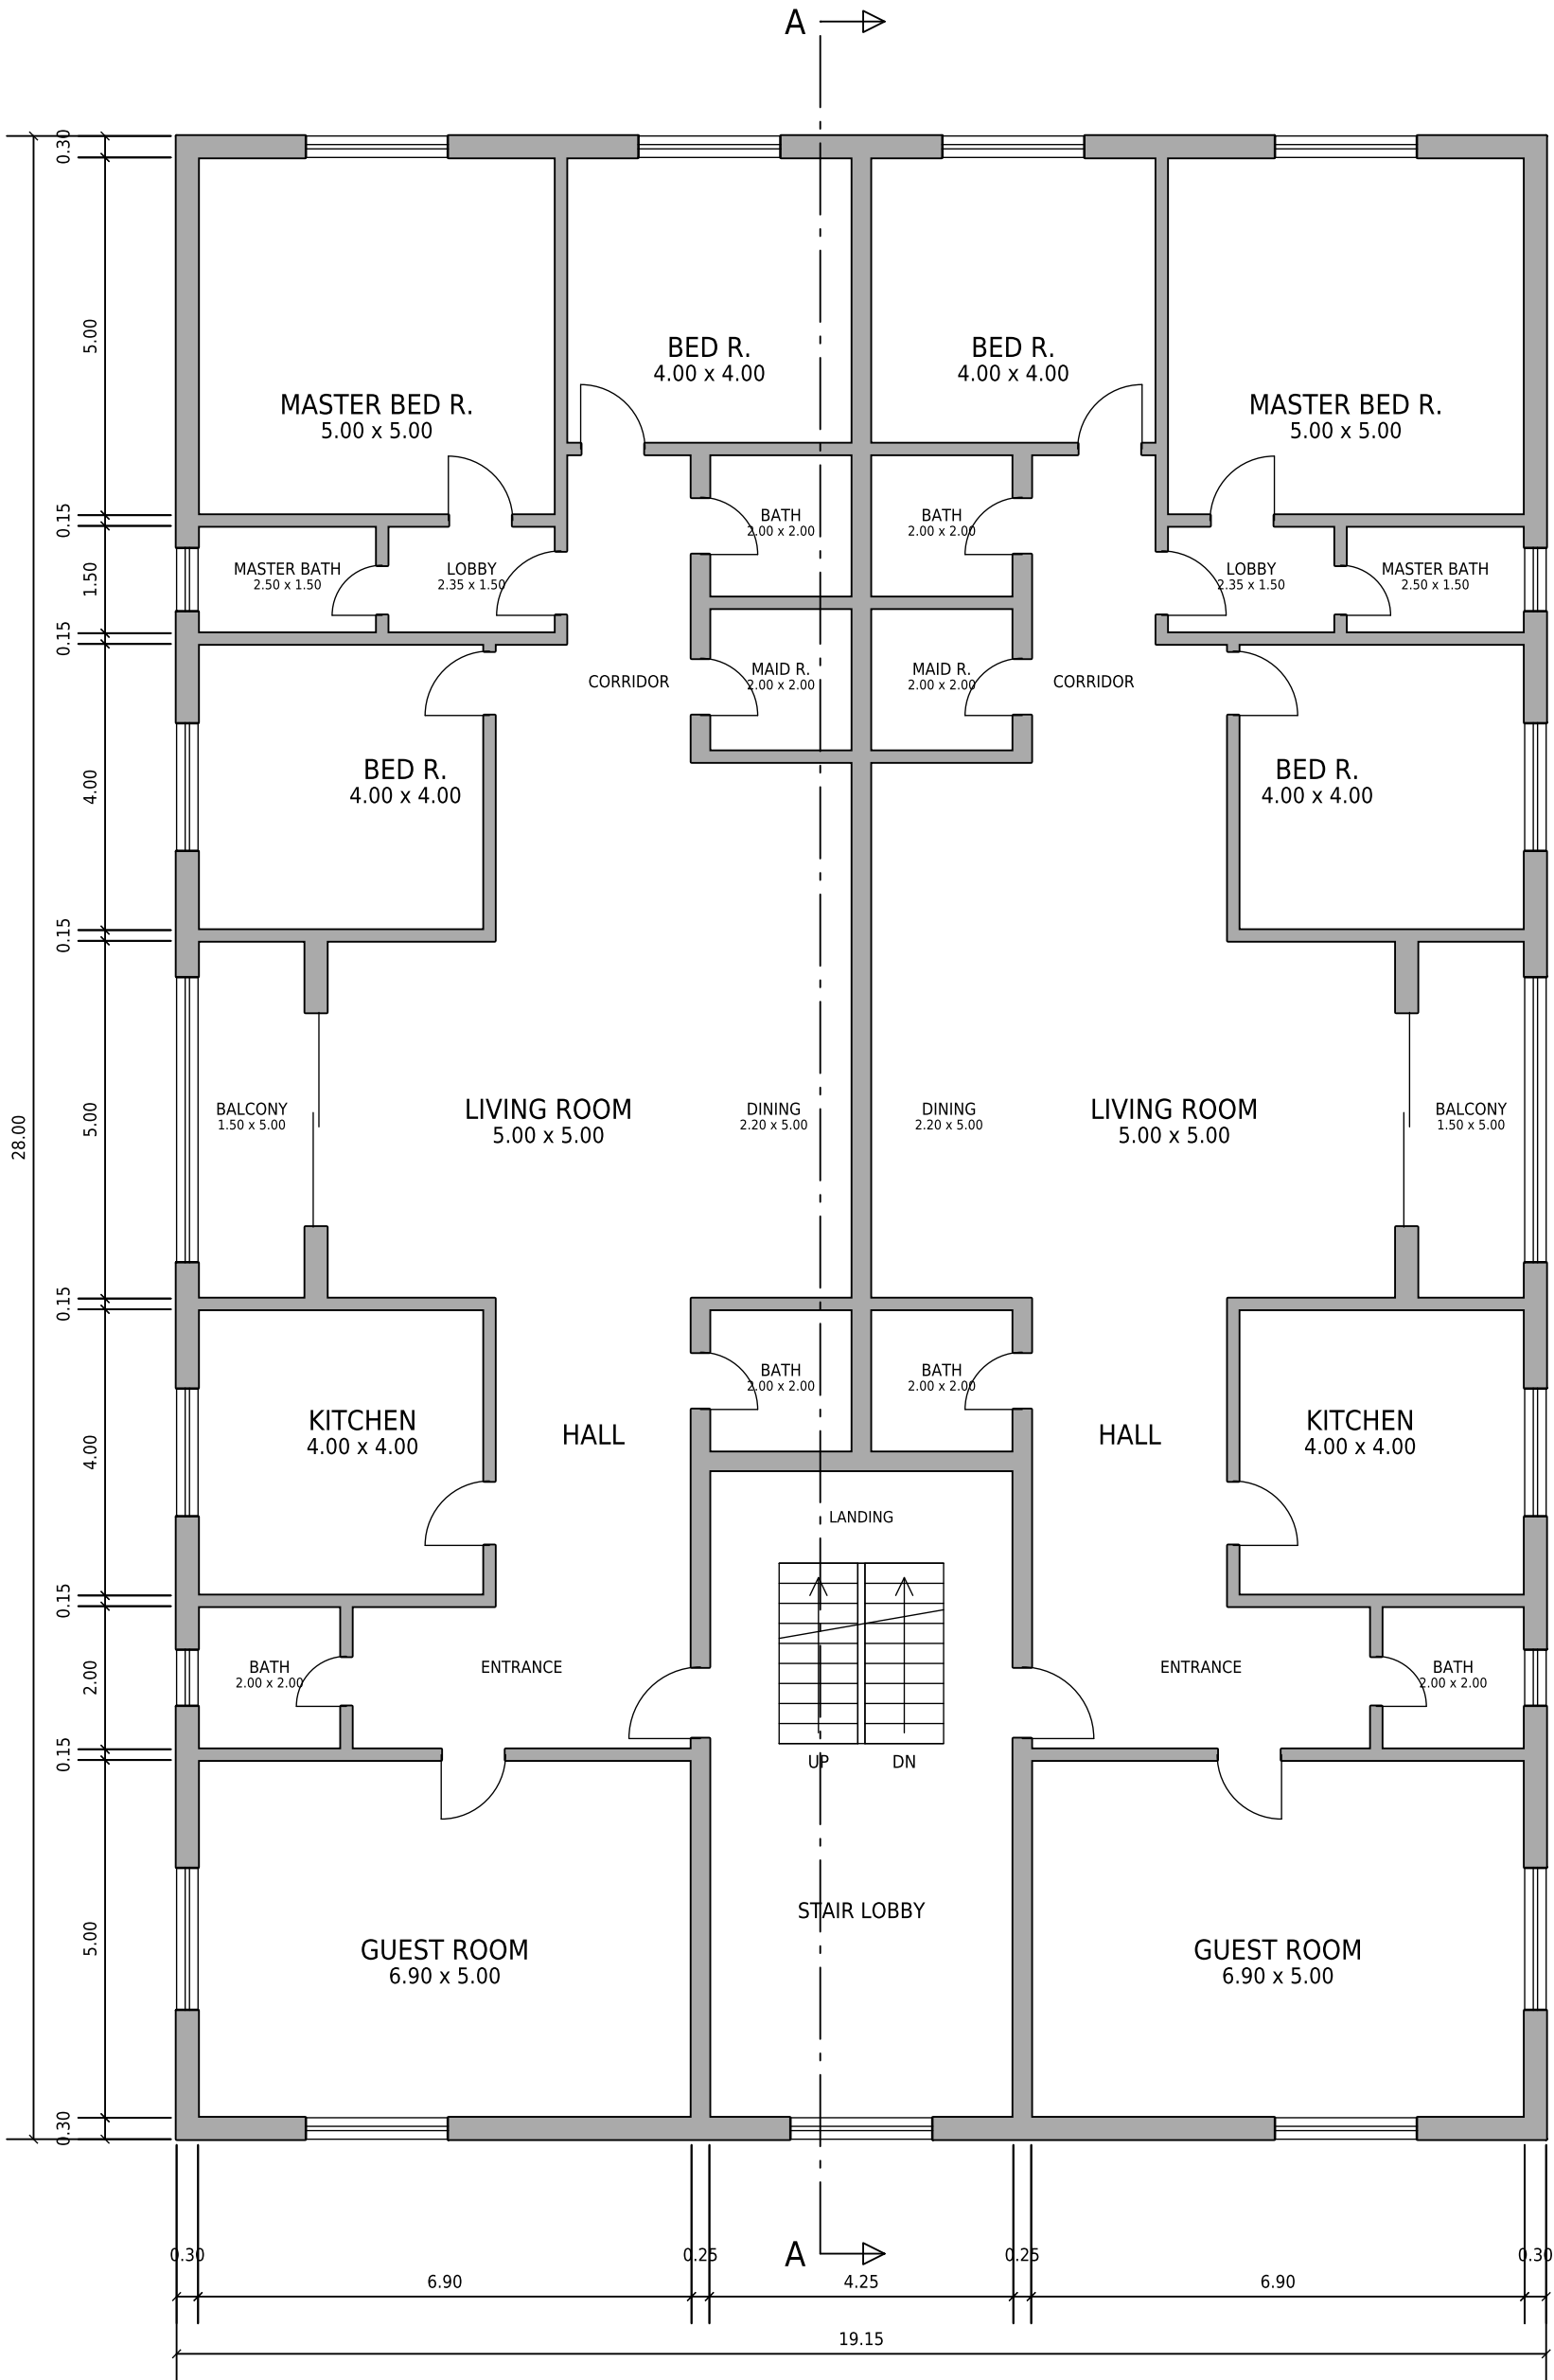


FIRST FLOOR PLAN

FFL +3.40 | Scale 1:100 | 2 apartments

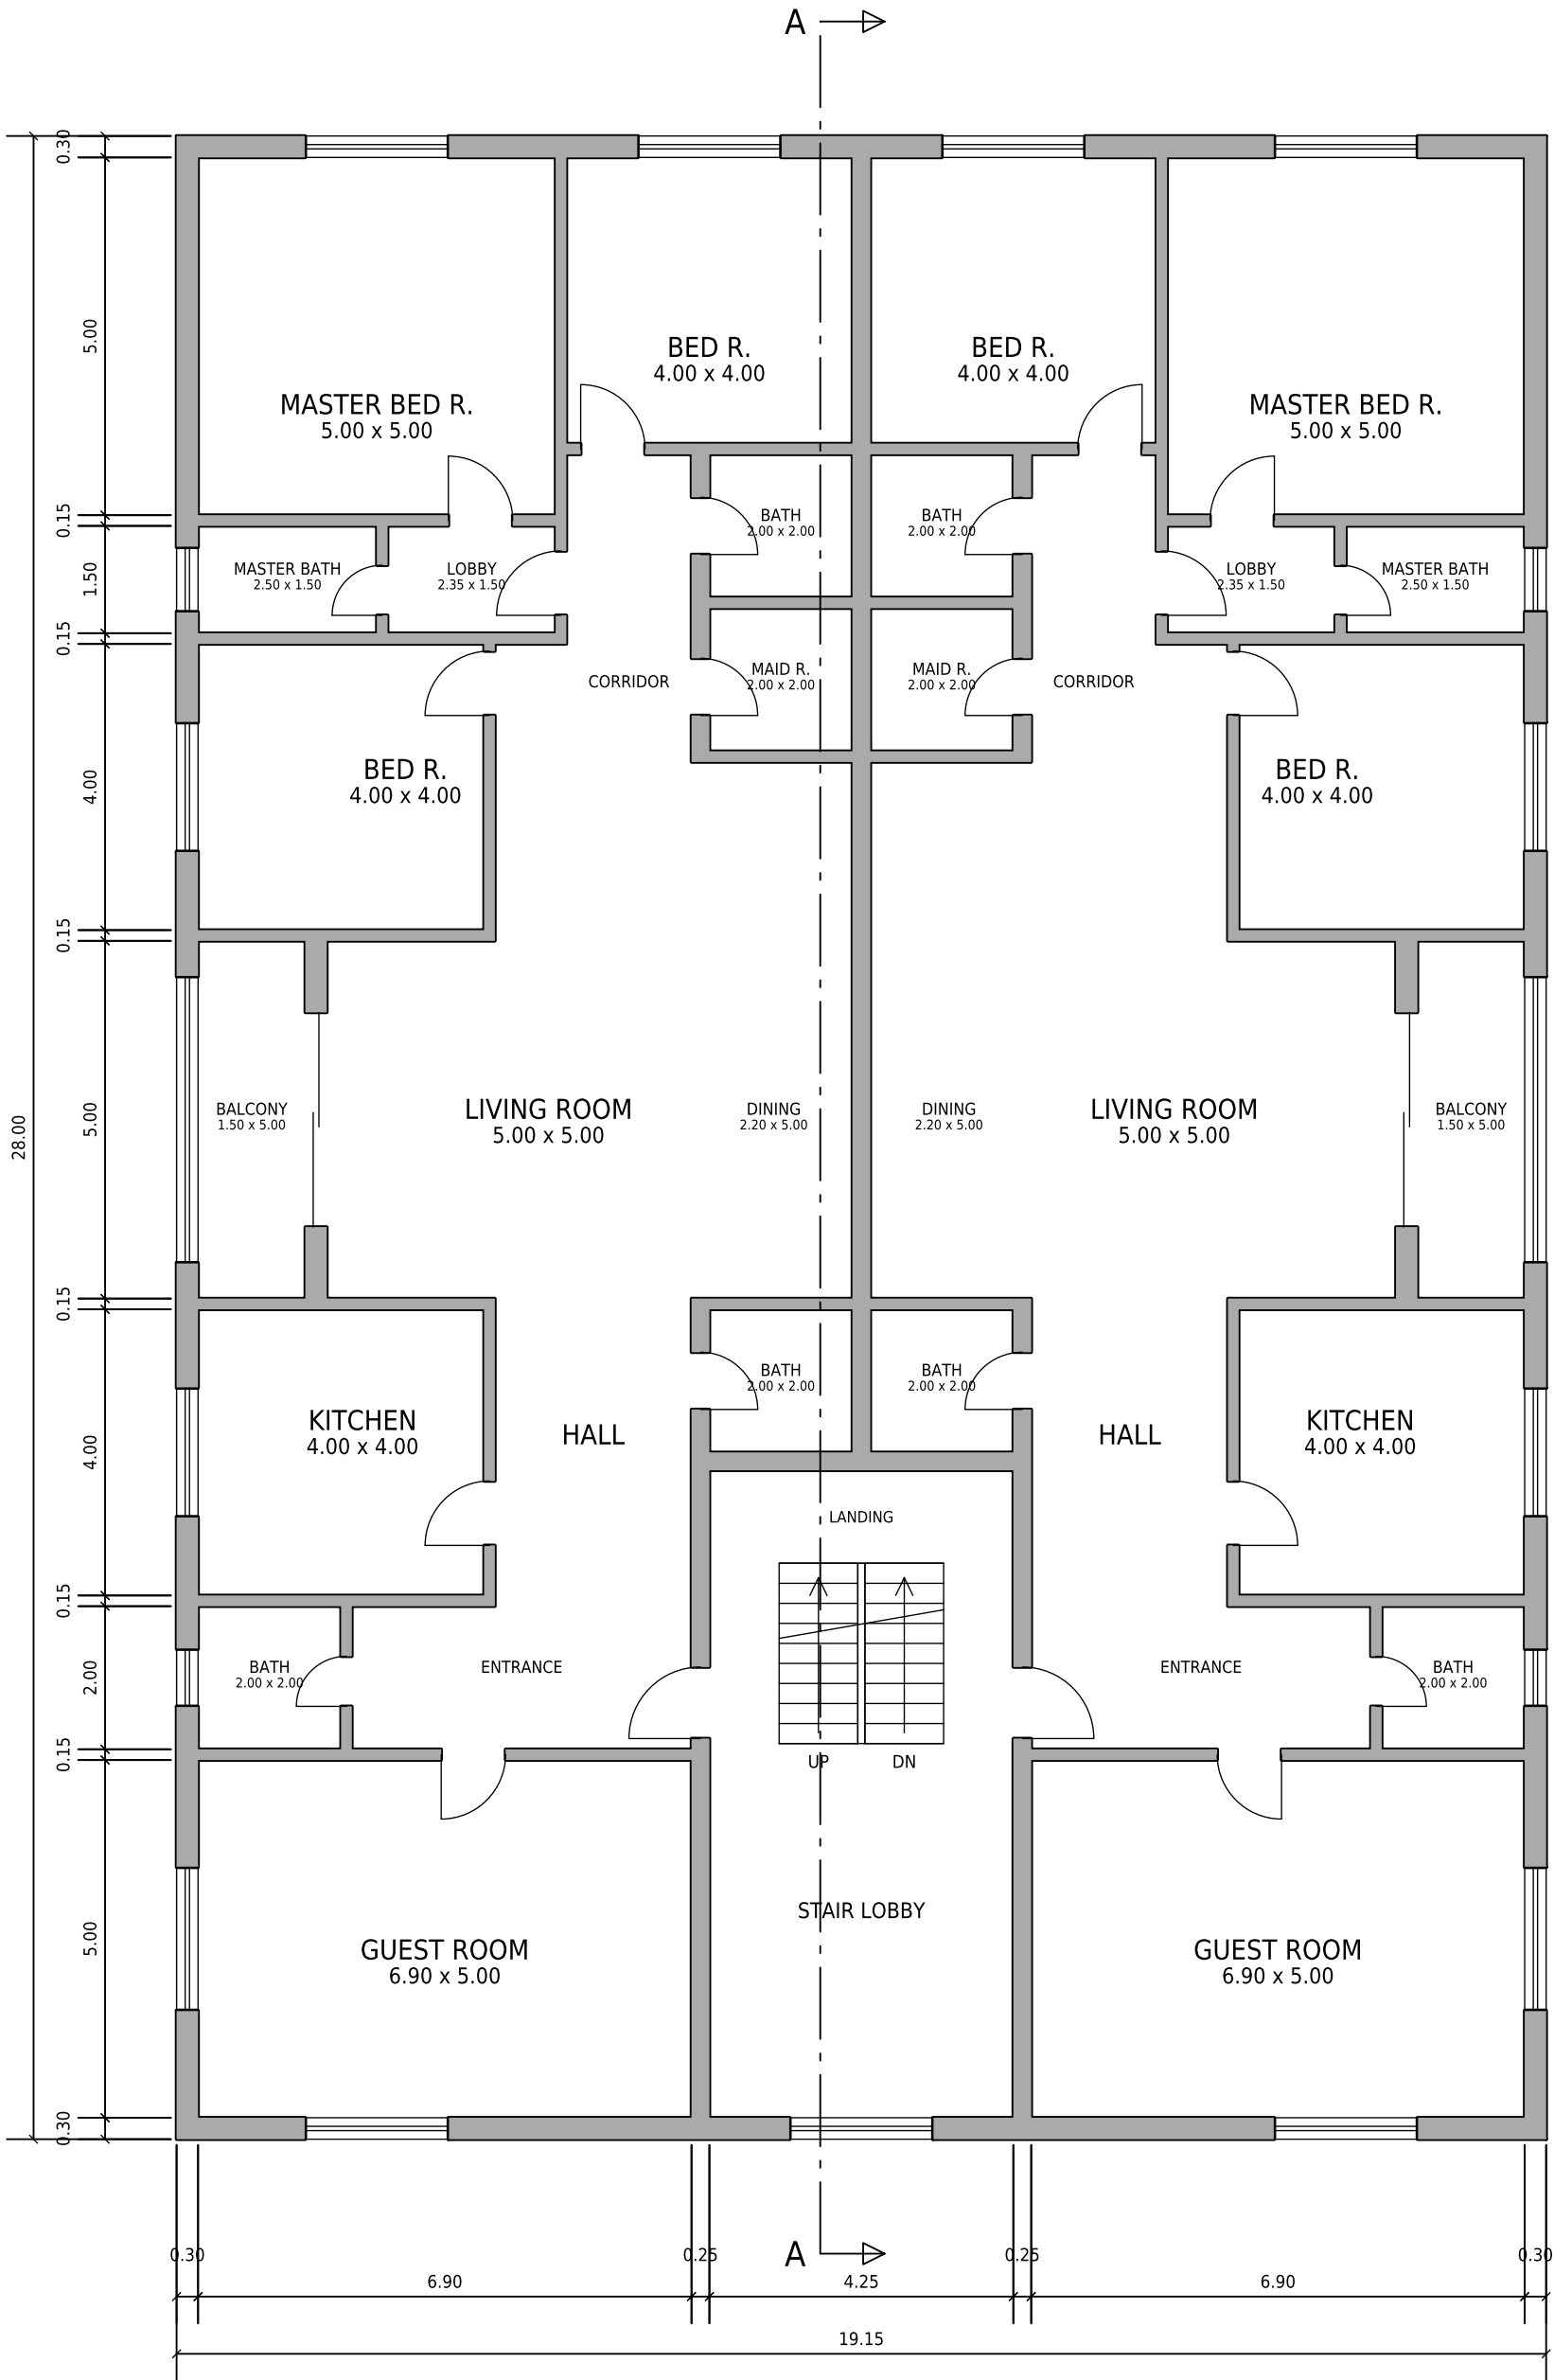


SECOND FLOOR PLAN

FFL +6.80 | Scale 1:100 | 2 apartments

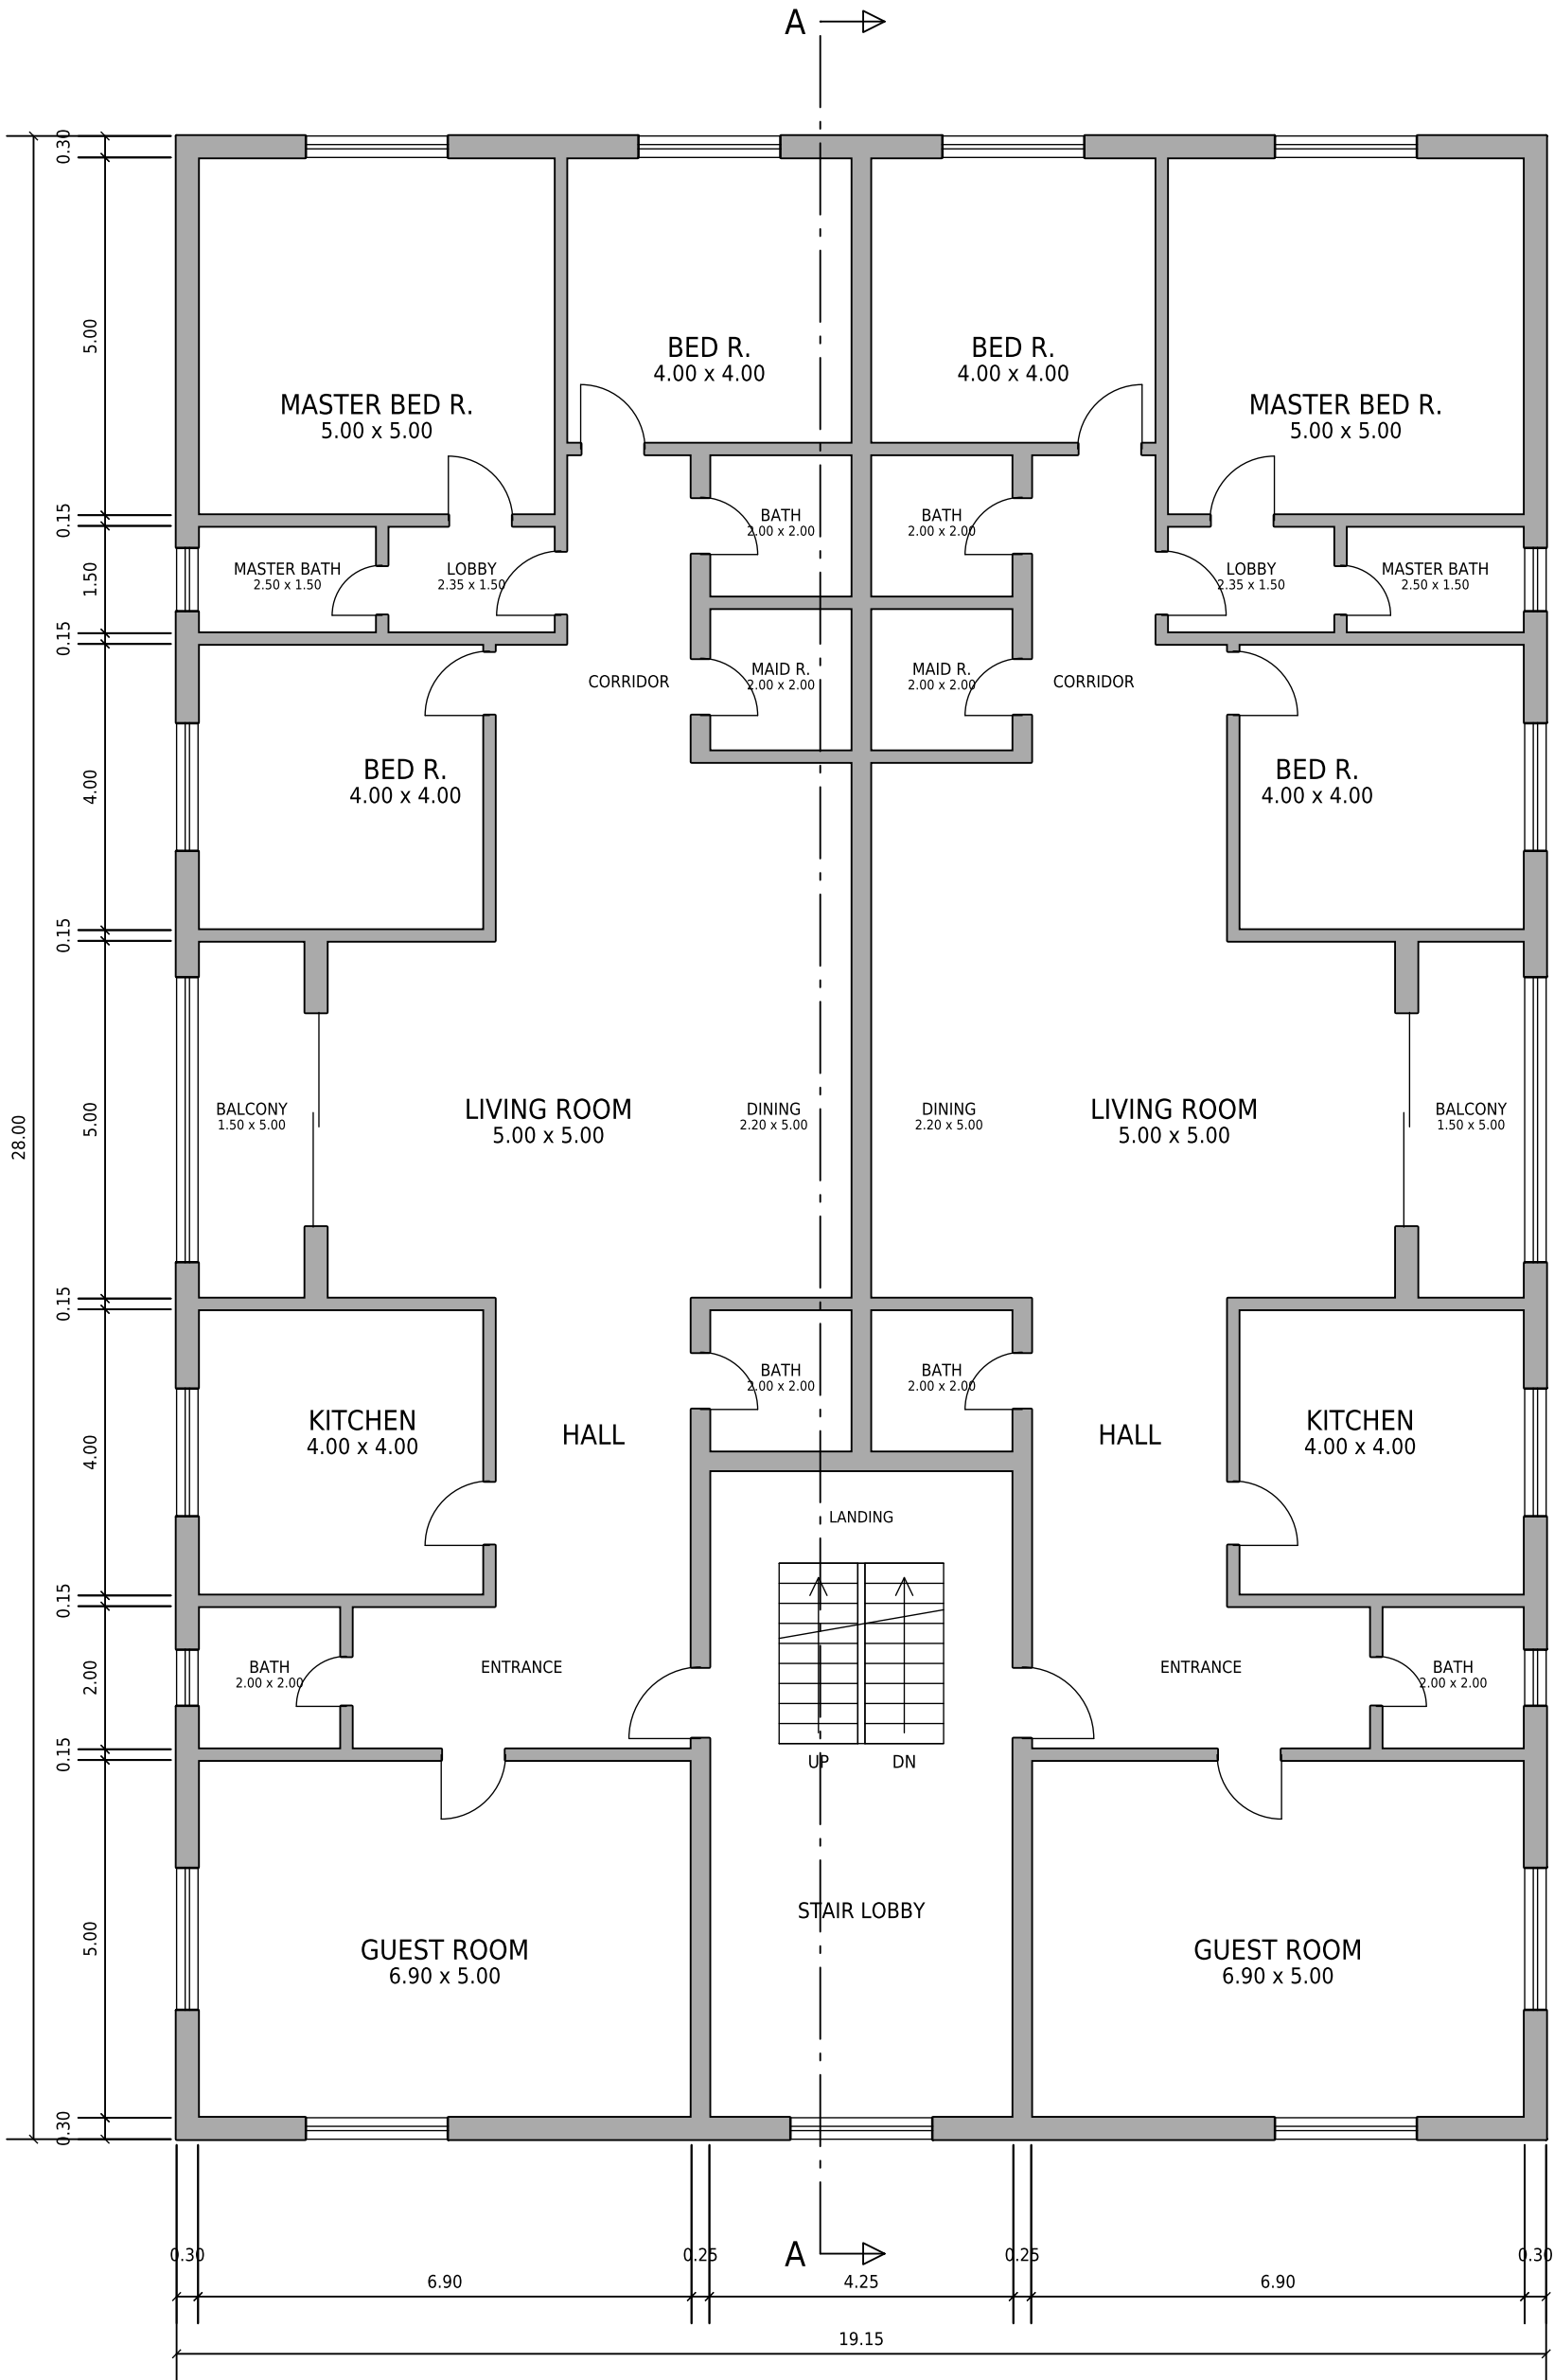


THIRD FLOOR PLAN

FFL +10.20 | Scale 1:100 | 2 apartments

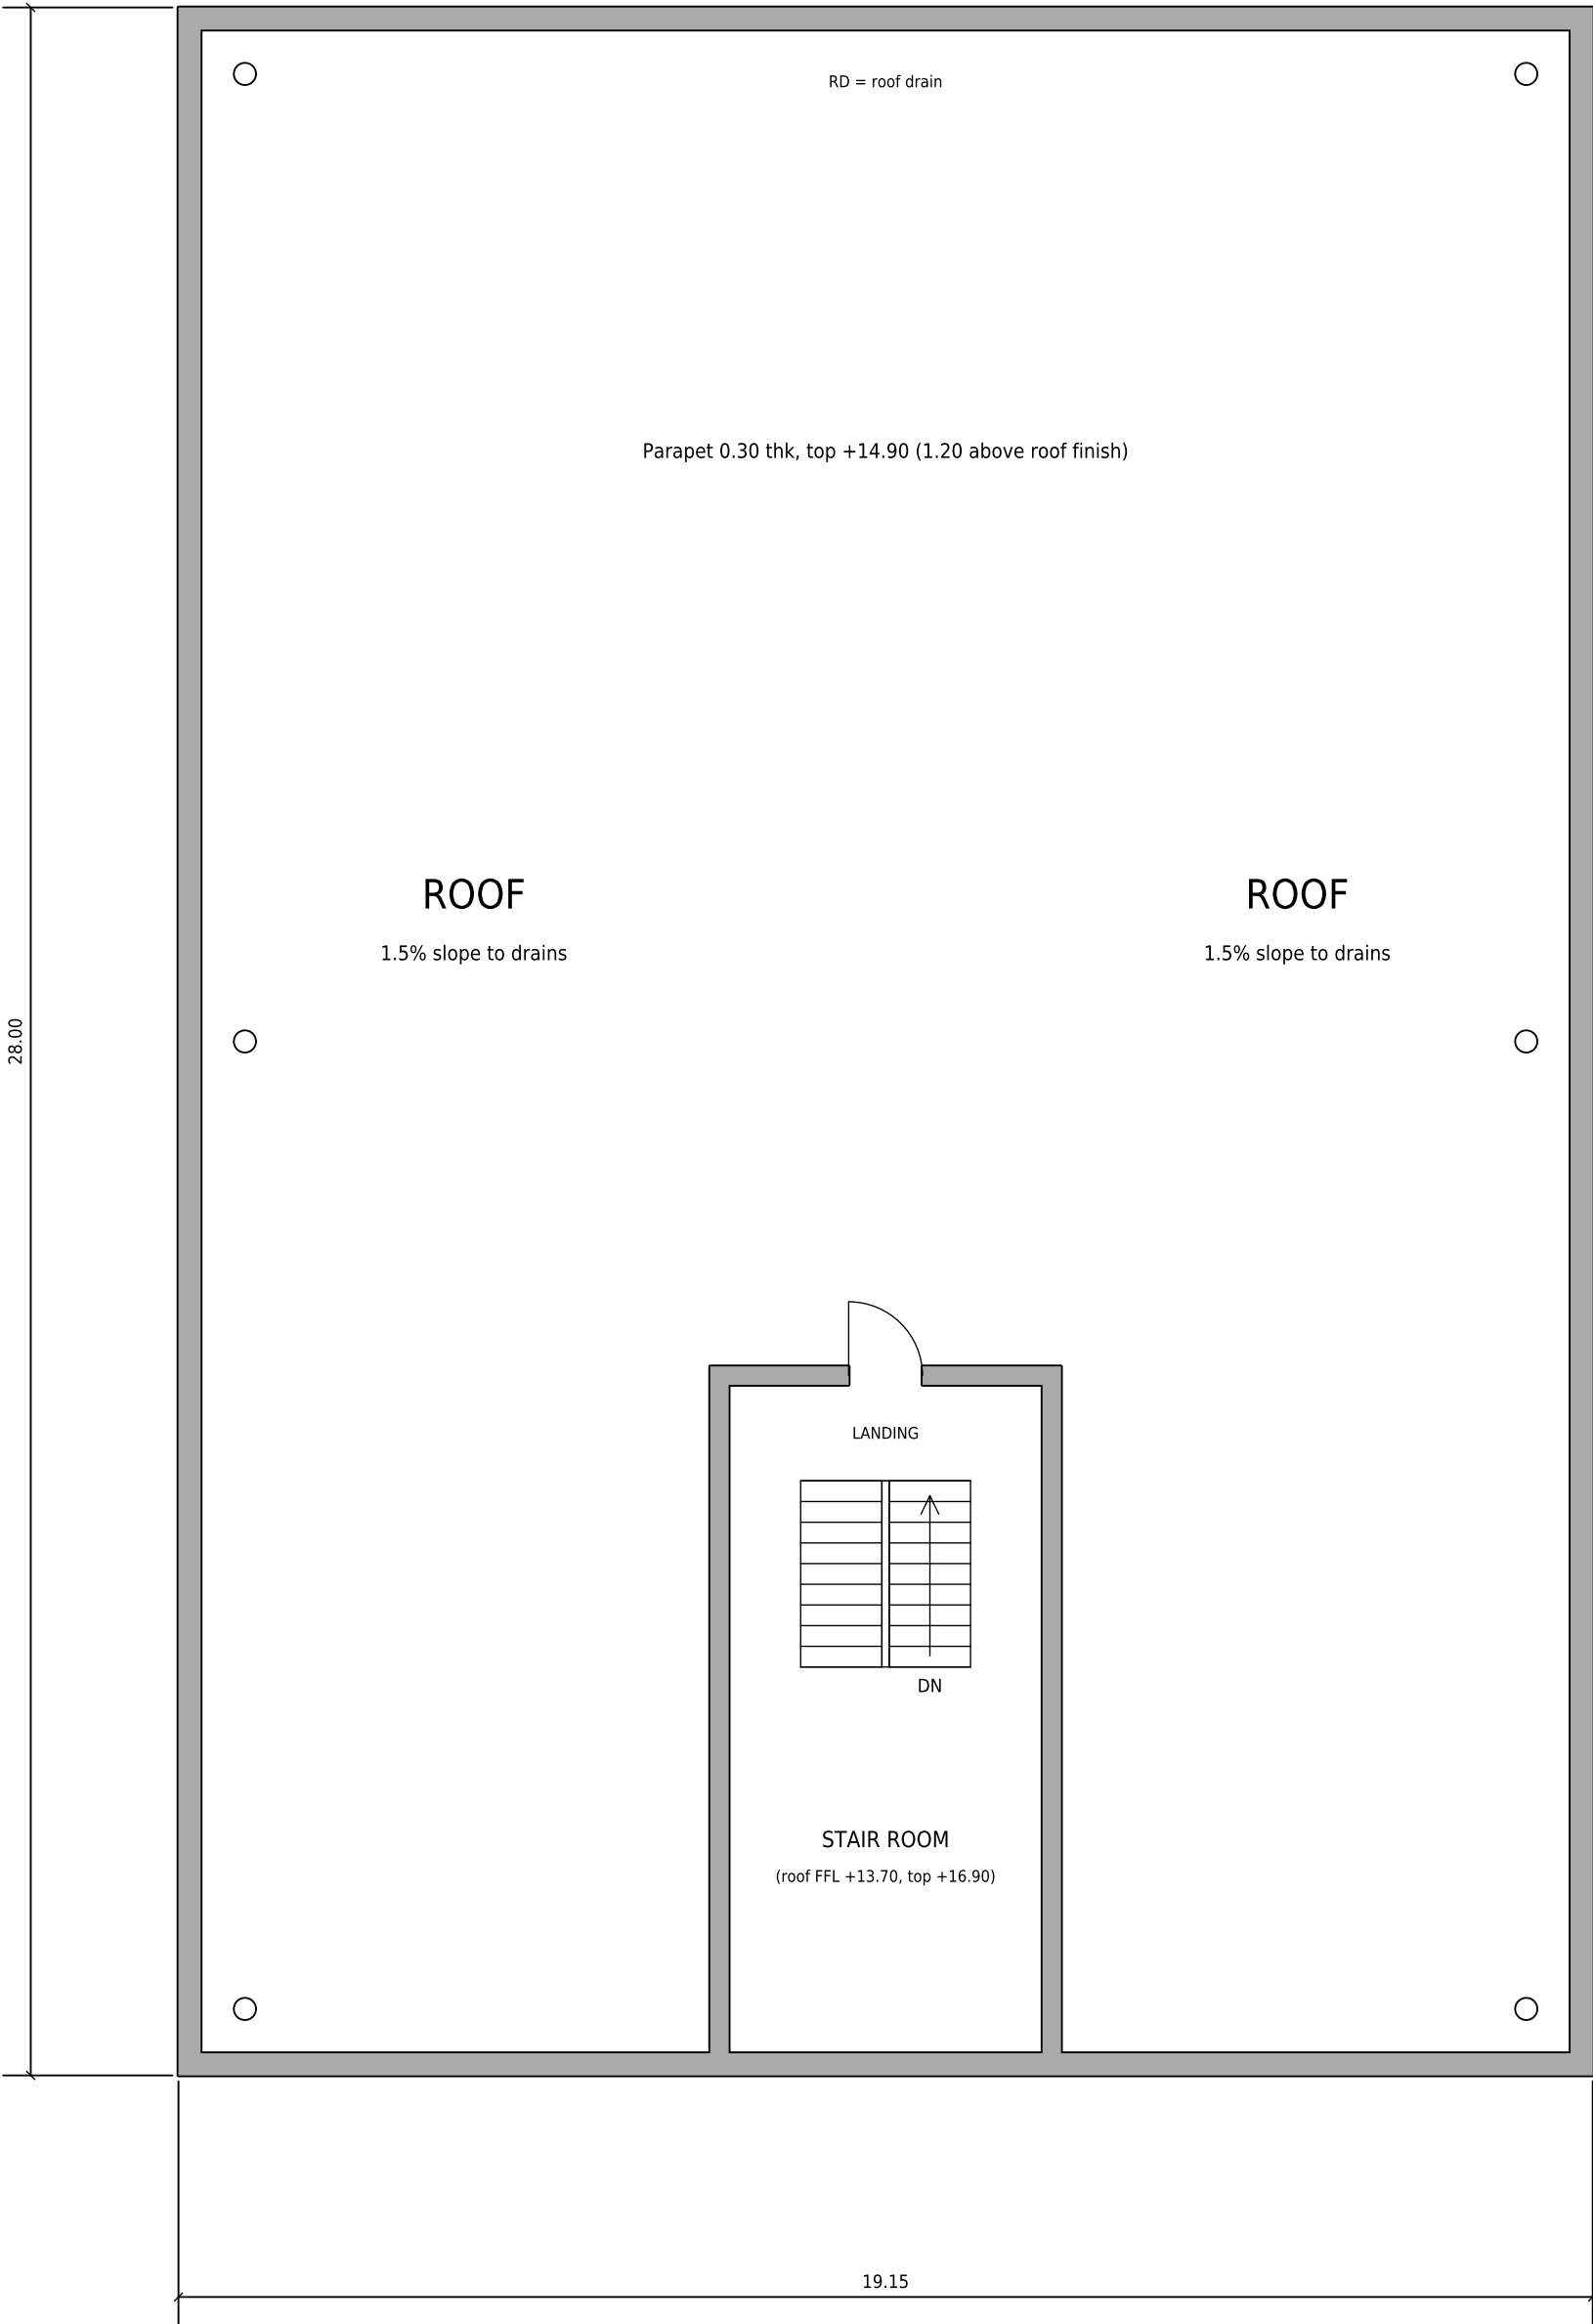


ROOF PLAN

Roof finish +13.70 | Scale 1:100

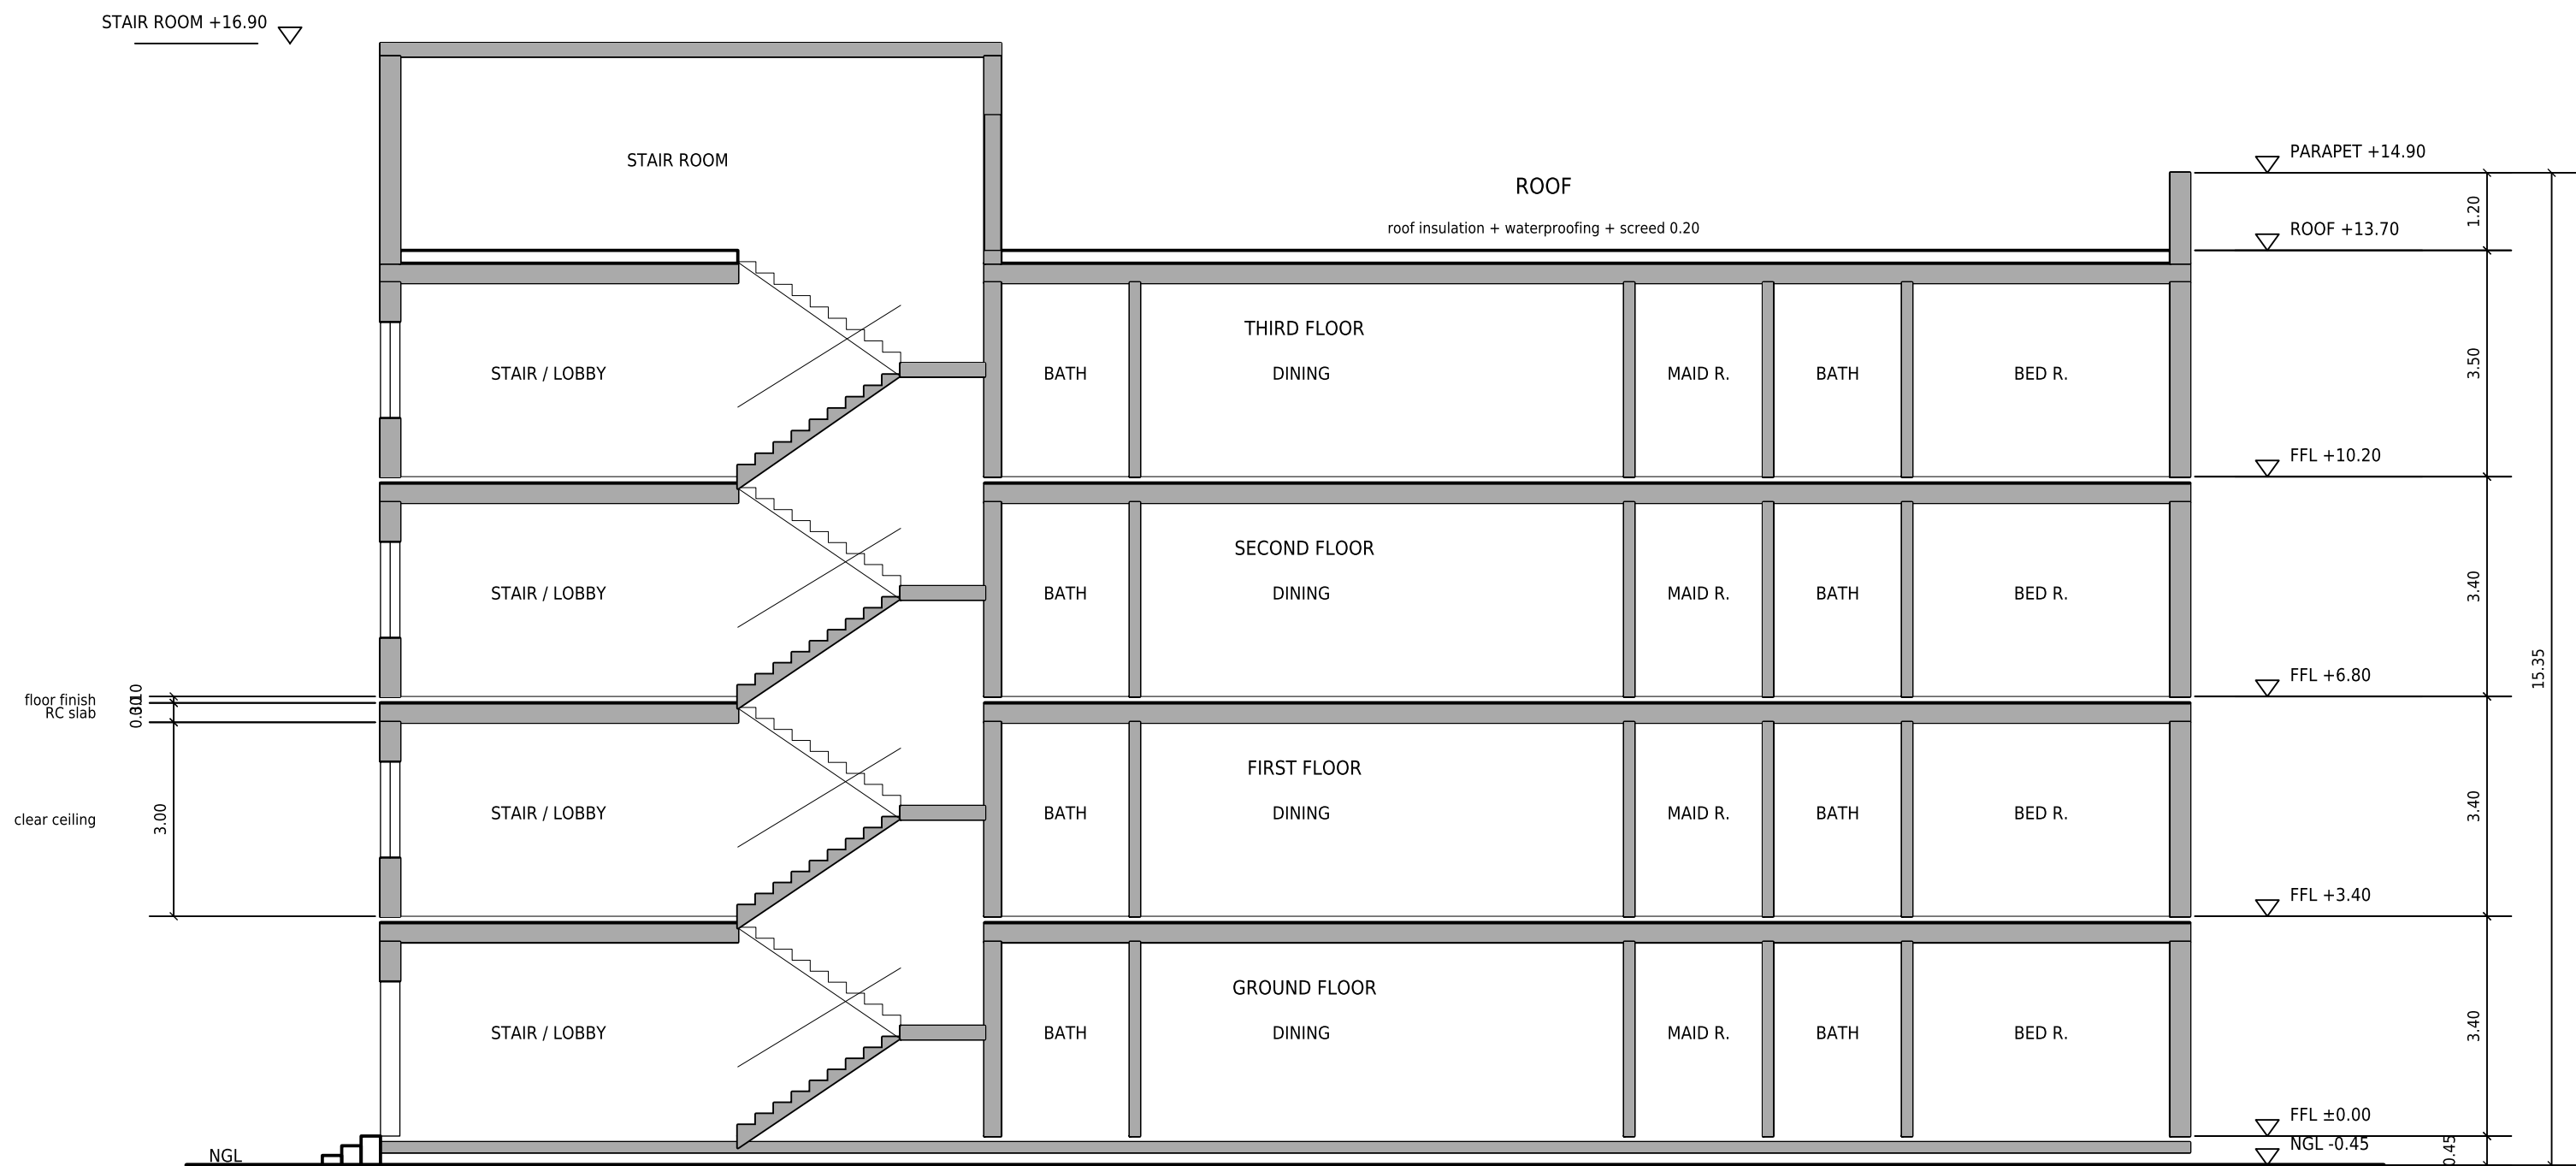

SECTION A-A

Scale 1:100 | looking east, cut through stair core

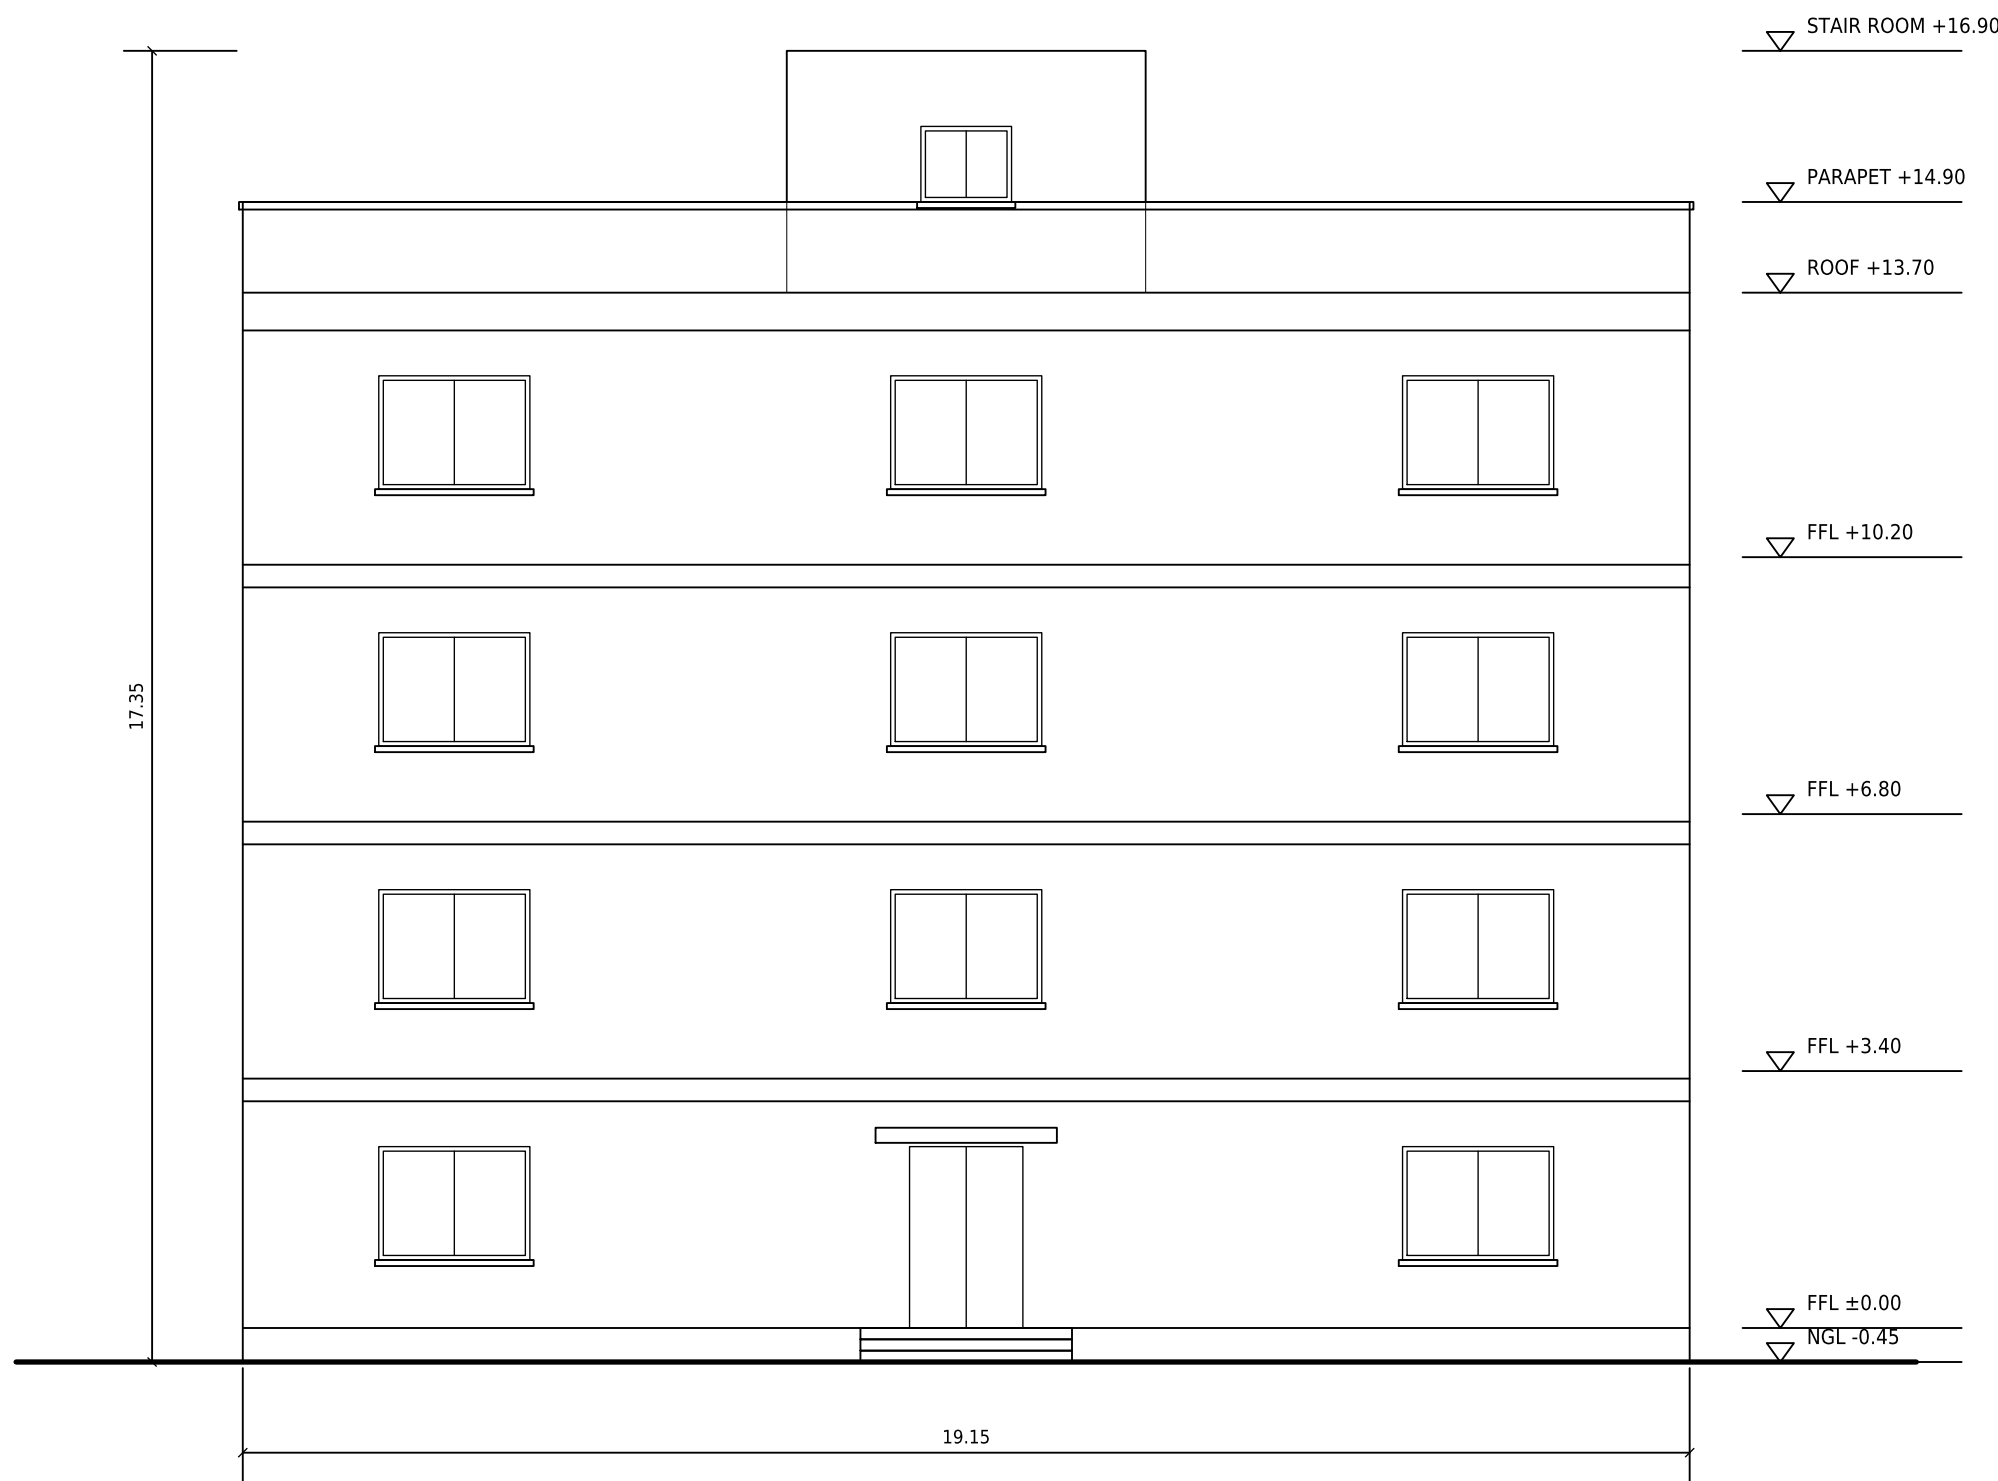

SOUTH ELEVATION (MAIN ENTRANCE)

Scale 1:100 | windows sill +0.90 / head +2.40 above each FFL

4-STOREY RESIDENTIAL BUILDING

8 apartments (2 mirrored units per floor) + common stair

VERTICAL DESIGN (SBC 201 / SBC 304)

Floor-to-floor height 3.40 m
Clear ceiling height 3.00 m (min. habitable 2.40)
Structural slab (ribbed/hordi) 0.30 m (l/18.5 for 5.3 m span)
Floor finish (screed + tiles) 0.10 m
Roof build-up 0.20 m + parapet 1.20 m
Ground FFL ± 0.00 = NGL +0.45 (3 steps x 0.15)

STAIR (SBC 201 means of egress)

20 risers x 0.170 m (max 0.18), tread 0.28 m (min 0.28)
Flight width 1.10 m, landing 1.30 m, handrail 0.90
Stair enclosure & unit walls 0.25 m, 1 h fire rated

WALLS

Exterior 0.30 insulated block (SBC 602)
Partitions 0.15

Units: metres | Verify with structural & energy calcs